
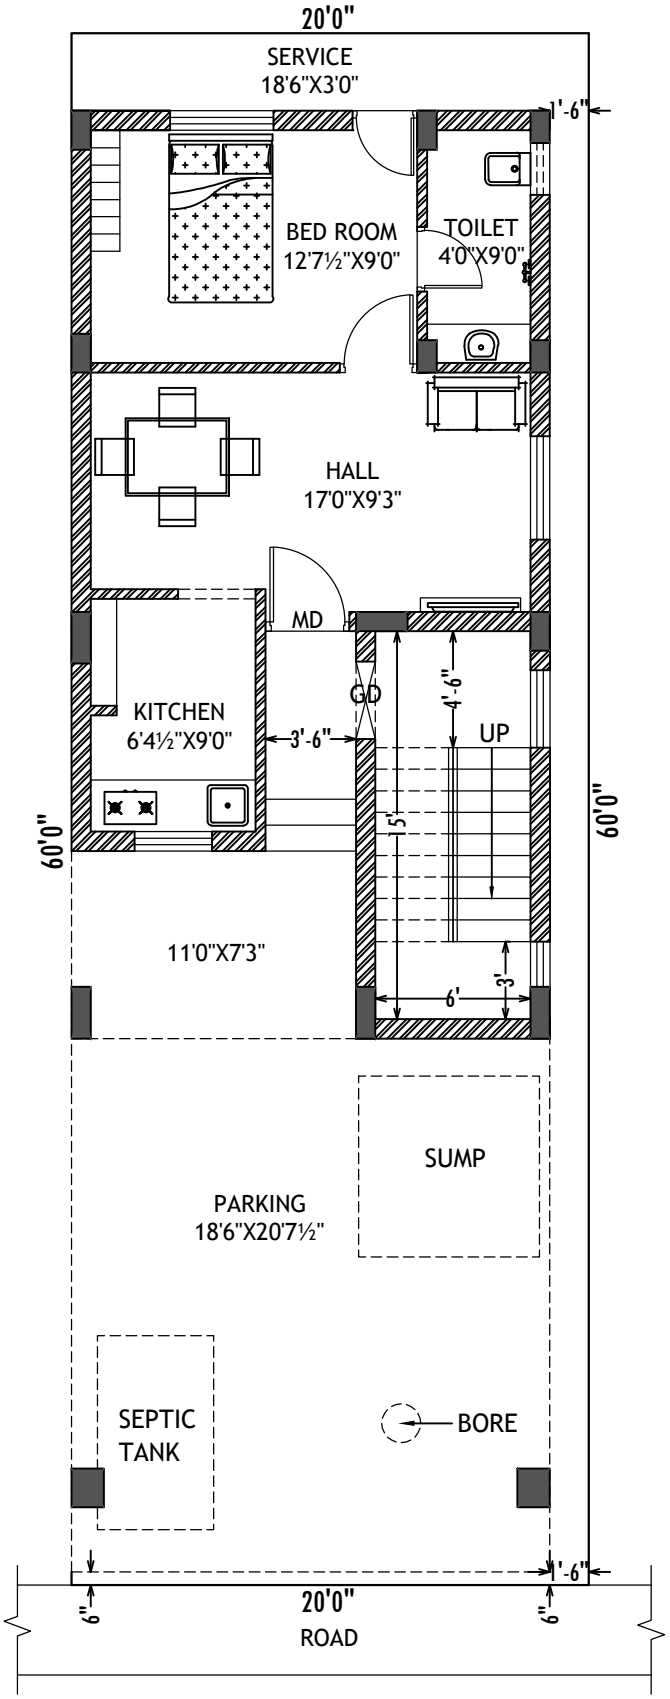



GROUND FLOOR PLAN

OWNER: Mr.SATHISH KUMAR	JOB NO : RT-S-13	W S N E	**KURAL-G** architect-engineers
PROJECT : PROPOSED RESIDENTIAL BUILDING AT KANDASAMY NAGAR, VANAGARAM.	DATE : 15-07-2026		\\Bharathi\d\M.PRAHARSHA\PH-SC-STR\JOB NO.1 SATHISH KUMAR\SATHISH KUMAR.dwg

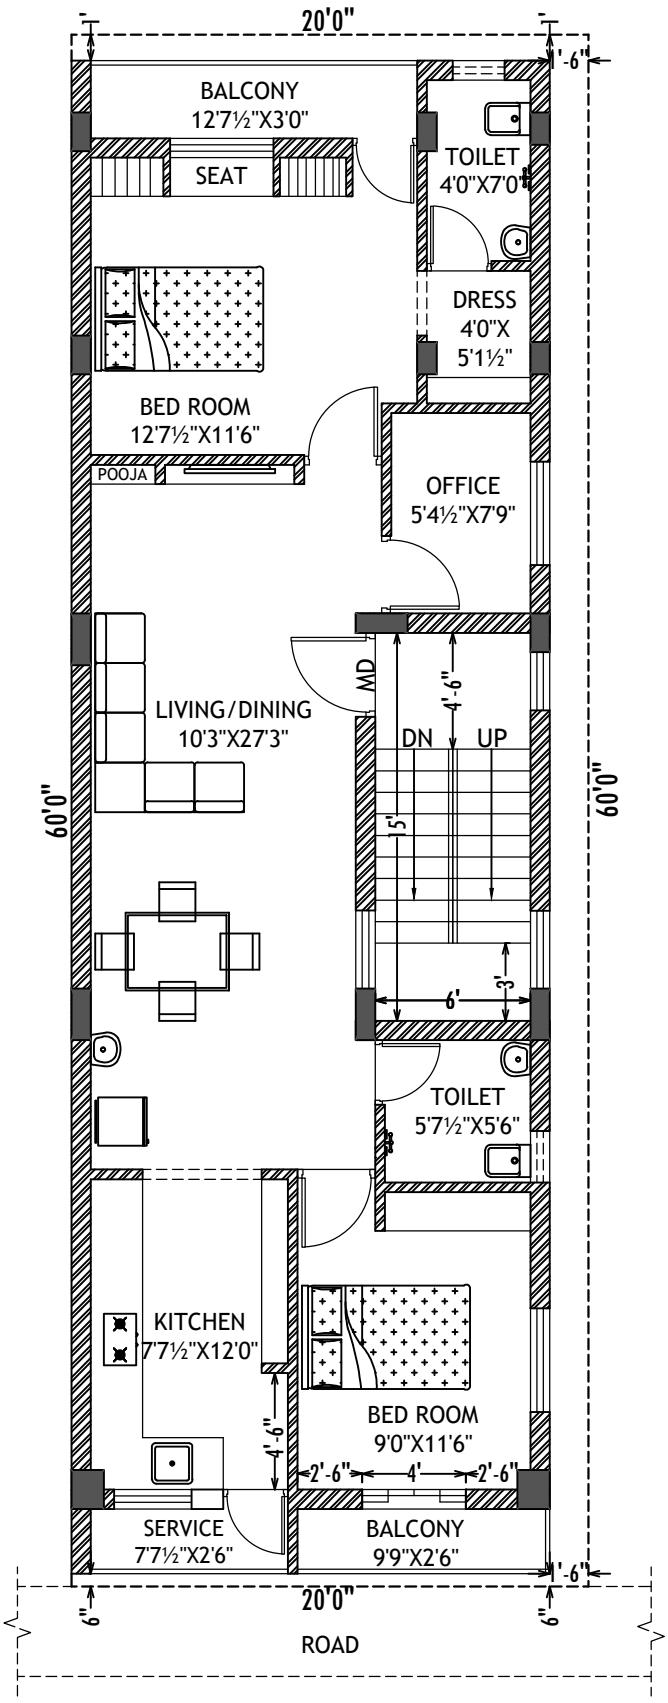


FIRST FLOOR PLAN

OWNER: Mr.SATHISH KUMAR	JOB NO : RT-S-13	W S N E	**KURAL-G** architect-engineers
PROJECT : PROPOSED RESIDENTIAL BUILDING AT KANDASAMY NAGAR, VANAGARAM.	DATE : 15-07-2026		\\Bharathi\d\M.PRAHARSHA\PH-SC-STR\JOB NO.1 SATHISH KUMAR\SATHISH KUMAR.dwg

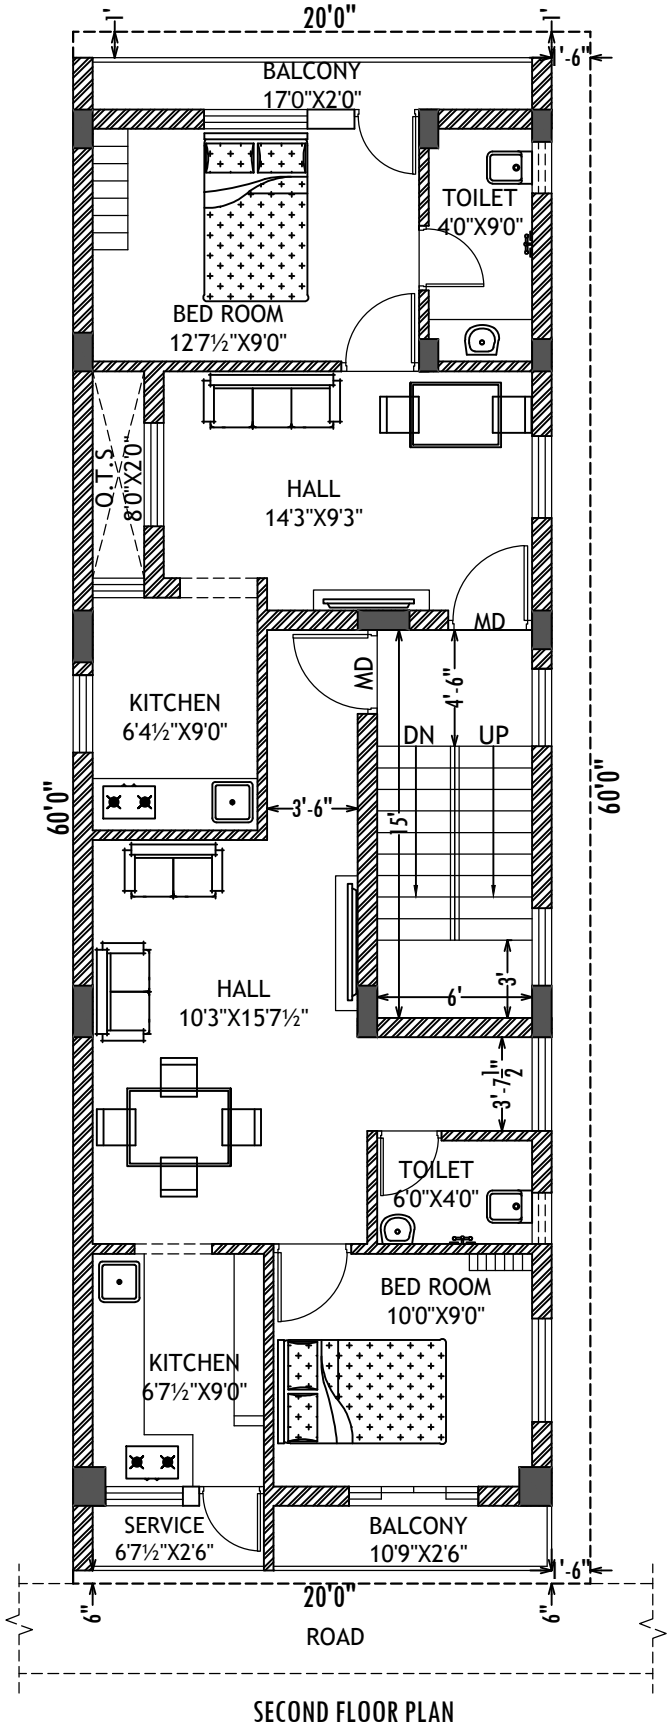

SECOND FLOOR PLAN


OWNER: Mr.SATHISH KUMAR	JOB NO : RT-S-13	W S N E	**KURAL-G** architect-engineers
PROJECT : PROPOSED RESIDENTIAL BUILDING AT KANDASAMY NAGAR, VANAGARAM.	DATE : 15-07-2026		\\Bharathi\d\M.PRAHARSHA\PH-SC-STR\JOB NO.1 SATHISH KUMAR\SATHISH KUMAR.dwg

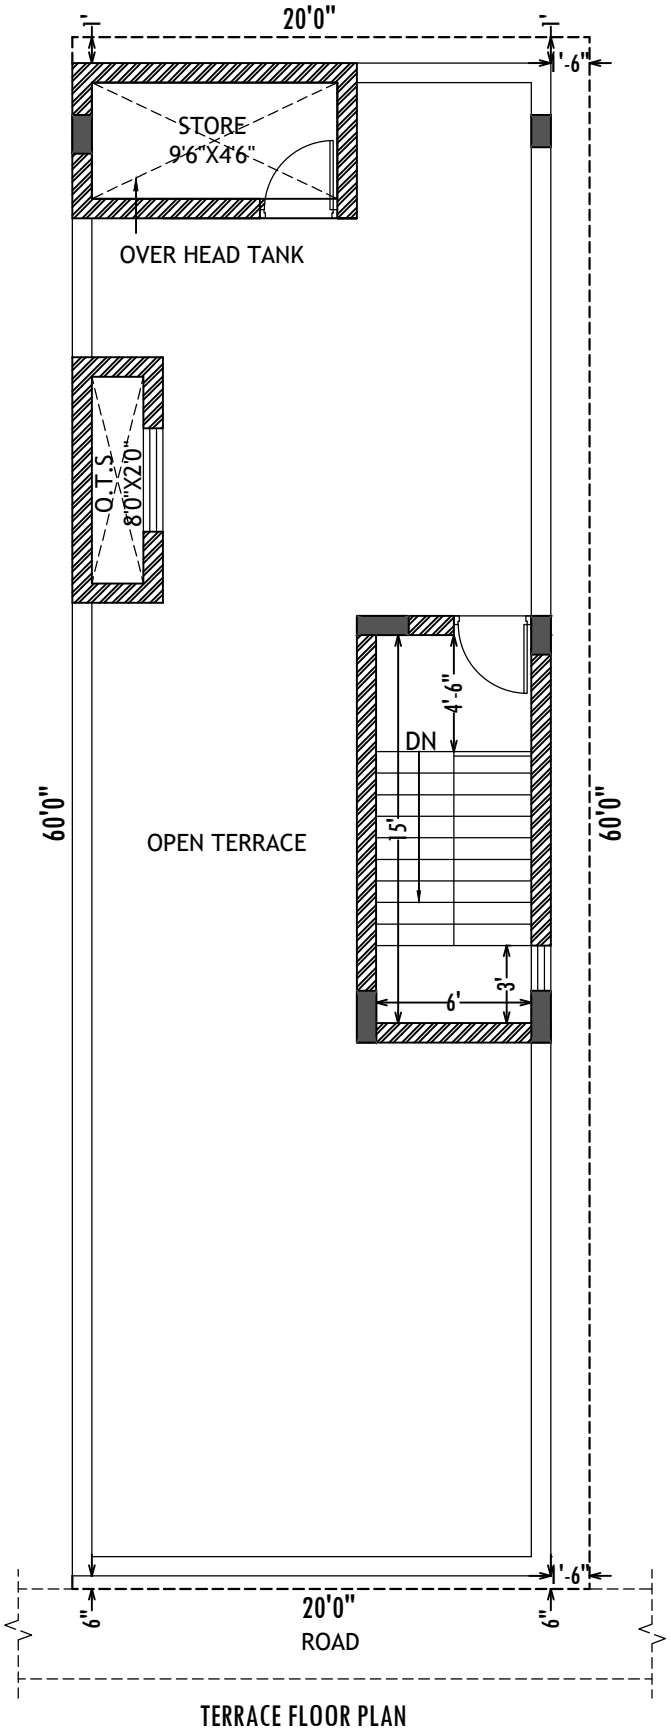

TERRACE FLOOR PLAN

OWNER: Mr.SATHISH KUMAR	JOB NO : RT-S-13	W S N E	**KURAL-G** architect-engineers
PROJECT : PROPOSED RESIDENTIAL BUILDING AT KANDASAMY NAGAR, VANAGARAM.	DATE : 15-07-2026		\\Bharathi\d\M.PRAHARSHA\PH-SC-STR\JOB NO.1 SATHISH KUMAR\SATHISH KUMAR.dwg

SHEET NO - 01
24-10-2026

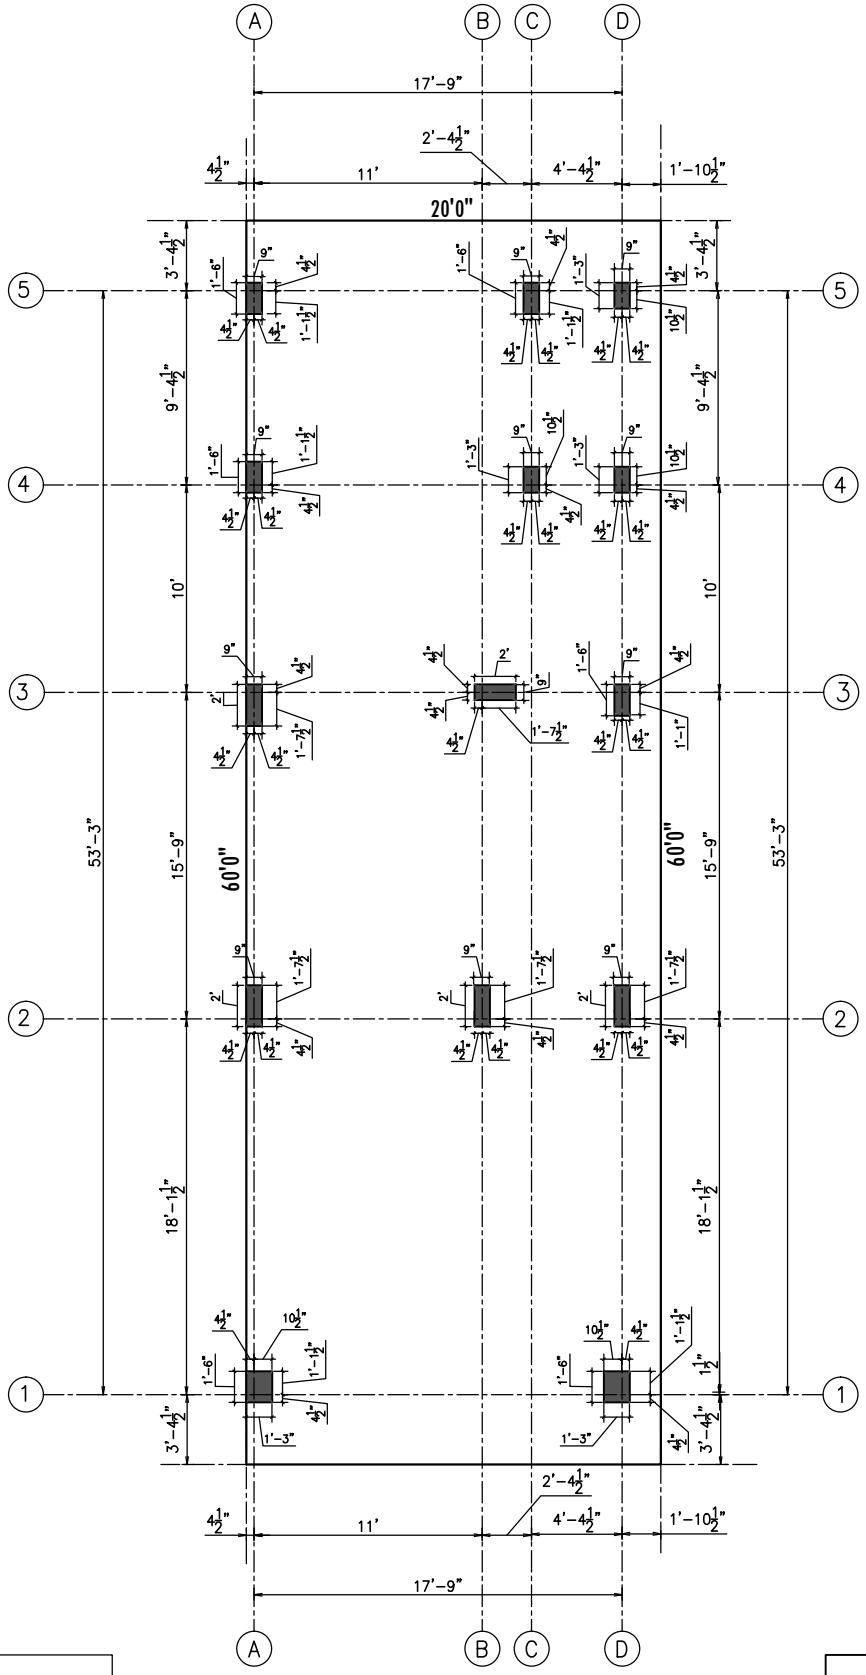



LEGEND

℄	:	CENTRE LINE
NGL	:	NATURAL GROUND LEVEL
FFL	:	FINISHED FLOOR LEVEL
TYP.	:	TYPICAL
■	:	COLUMN
—	:	COLUMN CENTERLINE
—	:	SITE BOUNDARY

LAYOUT OF FOOTING


KURAL-G
architect-engineers

JOB NO : PH–STR–01

CLIENT : SATHISH KUMAR

SITE : VANAGARAM

SHEET NO - 02
24-10-2026

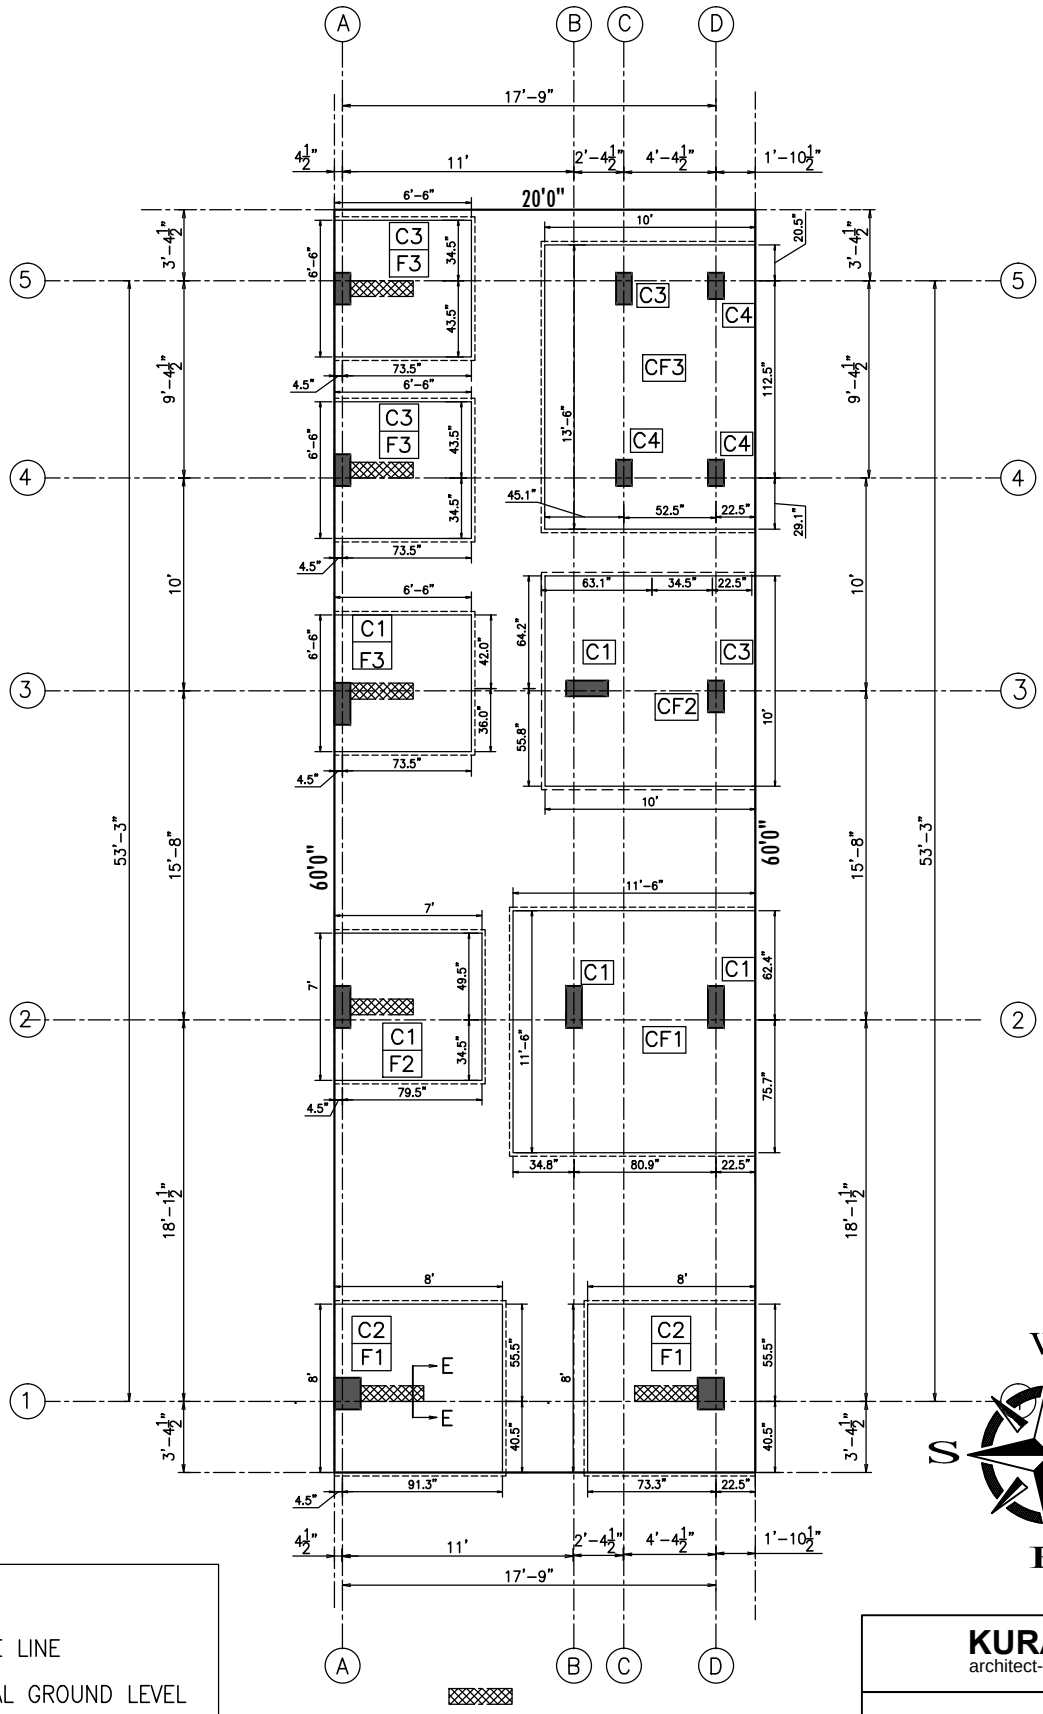

LEGEND

℄	:	CENTRE LINE
NGL	:	NATURAL GROUND LEVEL
FFL	:	FINISHED FLOOR LEVEL
TYP.	:	TYPICAL
■	:	COLUMN
——	:	COLUMN CENTERLINE
——	:	SITE BOUNDARY

LAYOUT OF FOOTING

KURAL-G architect-engineers
JOB NO : PH–STR–01
CLIENT : SATHISH KUMAR
SITE : VANAGARAM

SHEET NO - 03

24-10-2026

GENERAL NOTES:–

1. All dimenstion are in feet & inches.
2. Structural consultant not responsible for violation of any structural details
3. All laps should be staggered. (50xdia.)
4. Clear cover for:

a. Column = 40mm

5. Any descripencies should be immediately produced to the Engineer's notice before execution.

6.SBC 110 Kn/m2

MATERIAL STRENGTH

I. Grade of concrete – M25

II. Grade of steel – fe 500

NOTES:

1.REFER TYPICAL COLUMN DETAIL FOR CLARIFICATIONS ABOUT TIES AND LINKS SPACING.


2.REFERENCE DRAWINGS: SHEET–1, SHEET–2, SHEET–3, SHEET–5 AND LATEST ARCHITECTURAL DRAWINGS

FOOTINGS ARE DESIGNED ONLY FOR G+02 FLOORS.


As shown in Architectural drawing

LEGEND


- ℄ : CENTRE LINE
- NGL : NATURAL GROUND LEVEL
- FFL : FINISHED FLOOR LEVEL
- TYP. : TYPICAL
- ■ : COLUMN
- — : COLUMN CENTERLINE
- — : SITE BOUNDARY

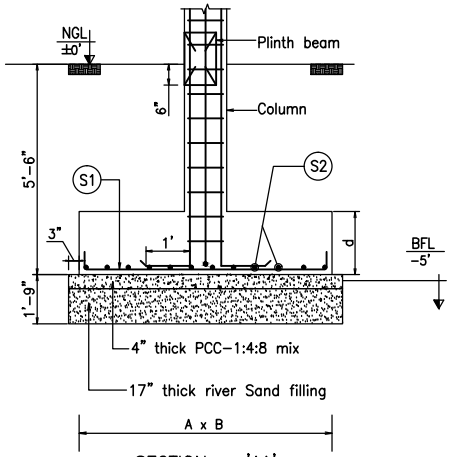


SECTION – 'AA'

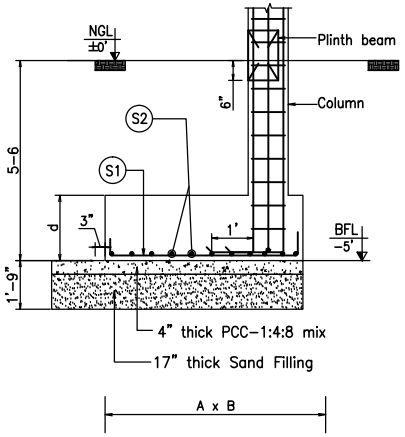


SECTION – 'CC'

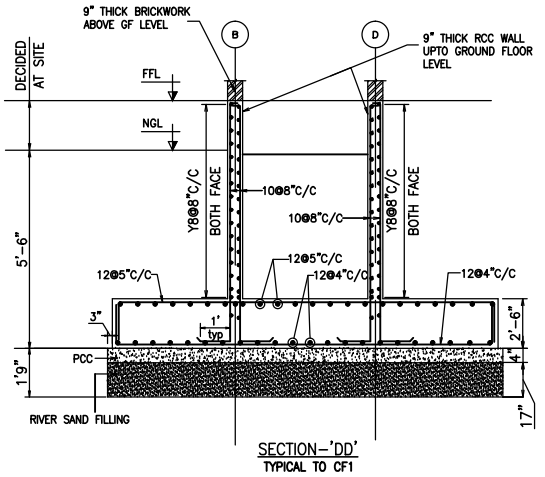


SECTION–'DD'
TYPICAL TO CF1

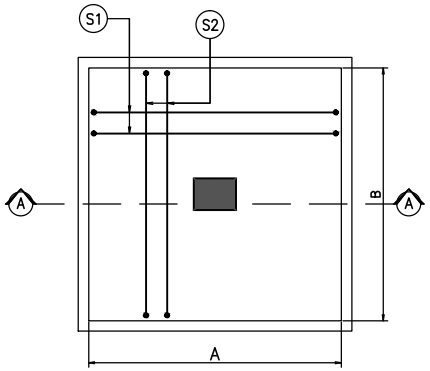

PLAN
TYPICAL FOOTING DETAIL
TYPE – 1

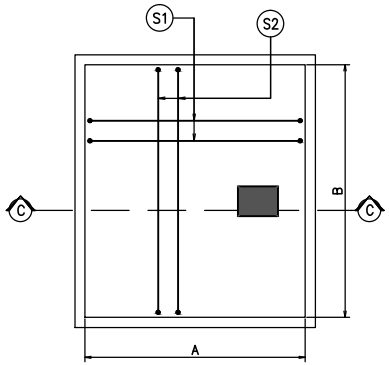


PLAN
TYPICAL FOOTING DETAIL
TYPE – 2

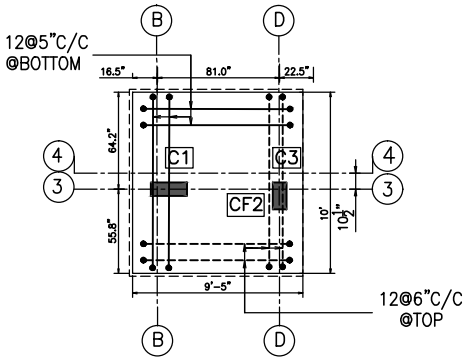



					TOP		BOTTOM		
					S1		S2		
F1	2	8'–0"	8'–0"	2'–0"	-----	-----	Y12@5"C/C	Y12@5"C/C	Type – 1
F2	1	7'–0"	7'–0"	1'–9"	-----	-----	Y12@5"C/C	Y12@5"C/C	Type – 1
F3	3	6'–6"	6'–6"	1'–9"	-----	-----	Y12@6"C/C	Y12@6"C/C	Type – 1
CF1	1	11'–6"	11'–6"	2'–6"	Y12@5"C/C	Y12@5"C/C	Y12@4"C/C	Y12@4"C/C	Type – 1
CF2	1	10'–0"	10'–0"	2'–6"	Y12@6"C/C	Y12@6"C/C	Y12@5"C/C	Y12@5"C/C	Type – 1
CF3	1	13'–6"	10'–6"	2'–6"	Y12@5"C/C	Y12@5"C/C	Y12@4"C/C	Y12@4"C/C	Type – 1

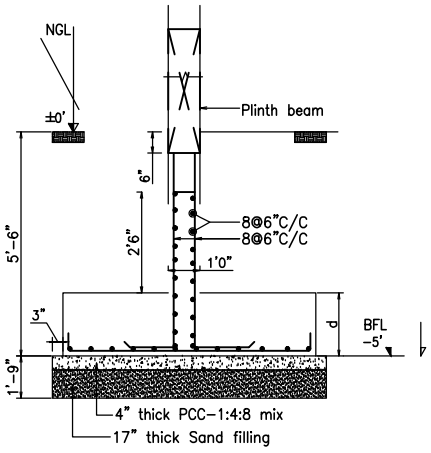

SECTION – 'EE'

KURAL-G
architect-engineers





JOB NO : PH–STR–01


CLIENT : SATHISH KUMAR

SITE :VANAGARAM


SHEET NO - 04

24-10-2026

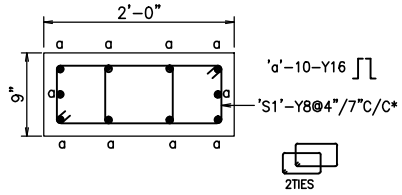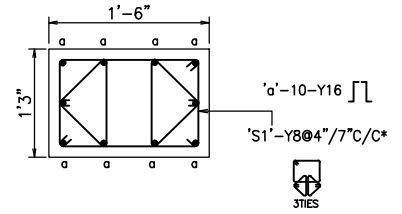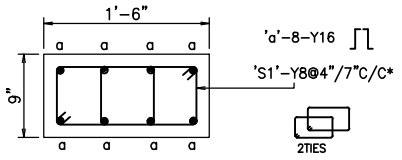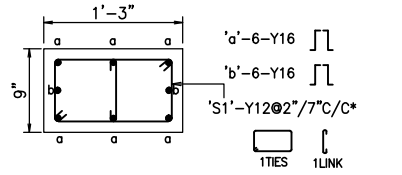
COLUMN NO.	NOS.	FROM GROUND FLOOR LEVEL TO TERRACE FLOOR LEVEL	REMARKS
C1	5		COLUMN SHALL BE TERMINATED AT TERRACE LEVEL
C2	2		COLUMN SHALL BE TERMINATED AT TERRACE LEVEL
C3	4		COLUMN SHALL BE TERMINATED AT TERRACE LEVEL
C4	3		COLUMN SHALL BE TERMINATED AT TERRACE LEVEL

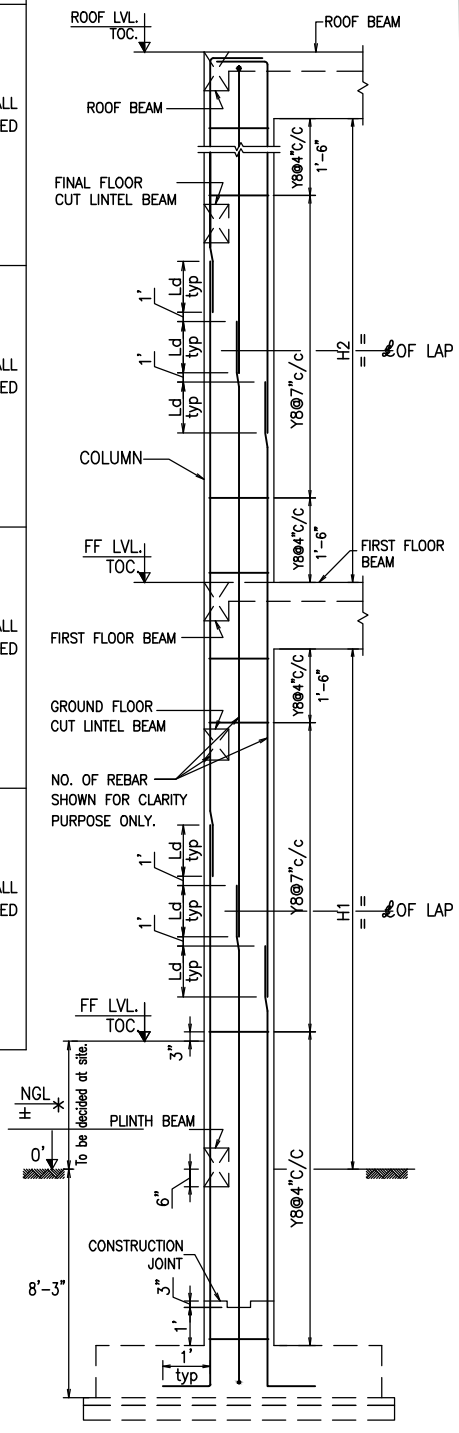

Typical column details.

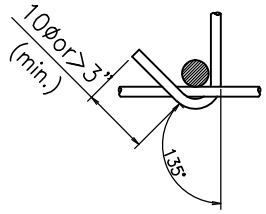

DETAIL–A (typ)

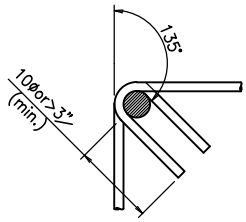

DETAIL–B (typ)

GENERAL NOTES:–

1. All dimenstion are in feet & inches.
2. Structural consultant not responsible for violation of any structural details
3. All laps should be staggered. (50xdia.)
4. Clear cover for:

a. Column = 40mm

5. Any descripencies should be immediately produced to the Engineer's notice before execution.

6.SBC 110 Kn/m2

MATERIAL STRENGTH

I. Grade of concrete – M25
II. Grade of steel – fe 500

As shown in Architectural drawing

COLUMNS ARE DESIGNED ONLY FOR G+02 FLOORS.

NOTES:
1.REFER TYPICAL COLUMN DETAIL FOR CLARIFICATIONS ABOUT TIES AND LINKS SPACING.
2.REFERENCE DRAWINGS:
SHEET–1, SHEET–2, SHEET–3, SHEET–4, SHEET–5, SHEET–6, AND LATEST ARCHITECTURAL DRAWINGS


KURAL-G
architect-engineers

JOB NO : PH–STR–01

CLIENT : SATHISH KUMAR

SITE :VANAGARAM

SHEET NO - 05
26-10-2026

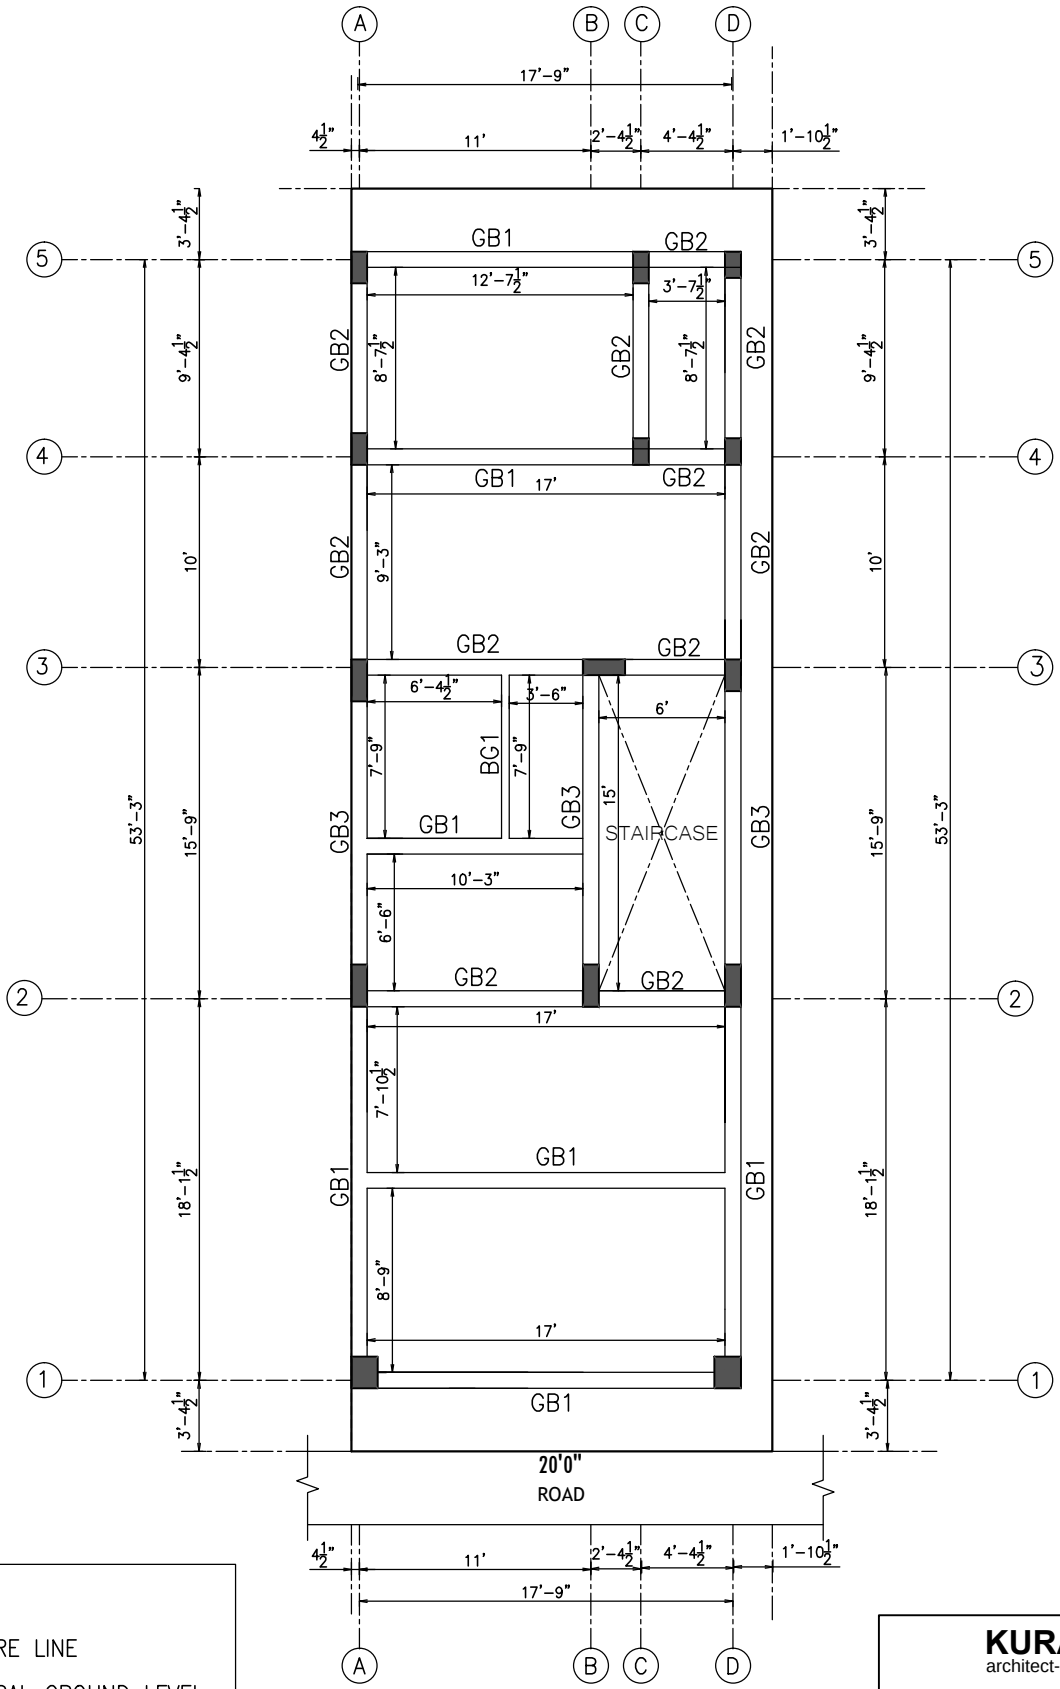



LEGEND

℄	:	CENTRE LINE
NGL	:	NATURAL GROUND LEVEL
FFL	:	FINISHED FLOOR LEVEL
TYP.	:	TYPICAL
■	:	COLUMN
—	:	COLUMN CENTERLINE
—	:	SITE BOUNDARY

LAYOUT OF GRADE BEAM NGL

KURAL-G
architect-engineers


JOB NO : PH–STR–01


CLIENT : SATHISH KUMAR

SITE : VANAGARAM


SHEET NO - 06

26-10-2026

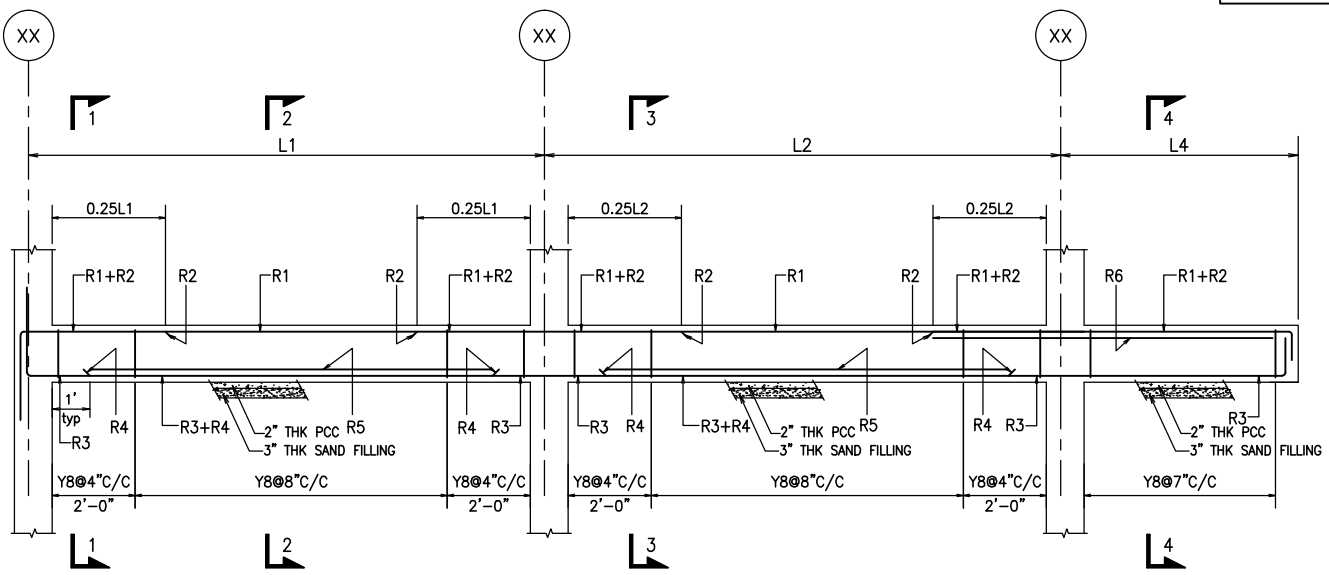


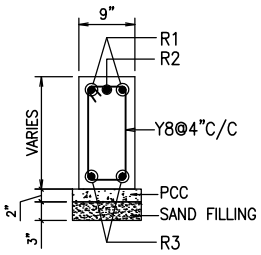


SECTION 1–1

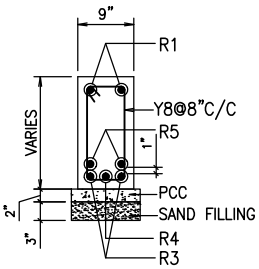


SECTION 2–2

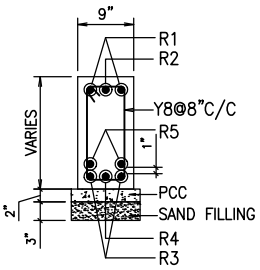

SECTION 3–3

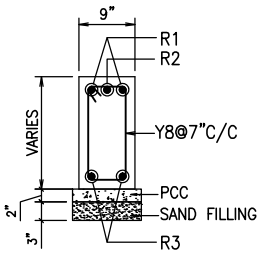


SECTION 4–4

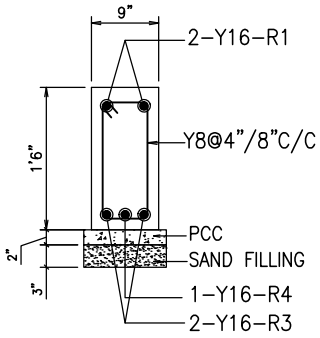


C.S OF GB1

[9"X1'–6"]

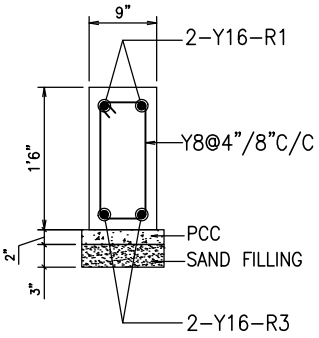


C.S OF GB2

[9"X1'–6"]

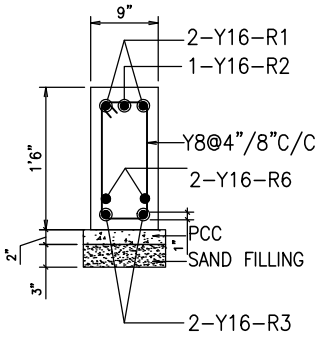

C.S OF GB3

[9"X1'–6"]

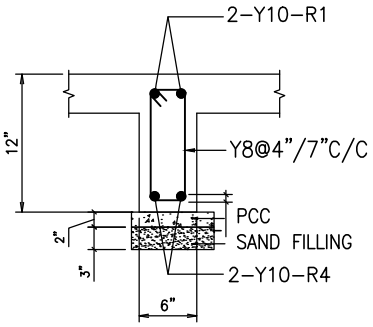

C.S OF BG1 AT FLOOR LEVEL

[6"X1'0"]

TYPICAL GRADE BEAM DETAILS

NOTE:

1. Clear cover = 30mm
2. All laps shall be 50ø
3. Top reinforcement shall be lapped at midspan and at support. bottom reinforcement
4. 3" thick sand and pcc layers shall be laid below all beams.

LEGEND

- ℄ : CENTRE LINE
- NGL : NATURAL GROUND LEVEL
- FFL : FINISHED FLOOR LEVEL
- TYP. : TYPICAL
- ■ : COLUMN
- — : COLUMN CENTERLINE
- — : SITE BOUNDARY

NOTE:

AT INTERIOR BEAM COLUMN JUNCTIONS THE TOP REINFORCEMENT PROVIEDED MUST BE MAXIMUM OF THE TWO BEAMS MEETING AT THAT JUNCTION.




KURAL-G
architect-engineers

JOB NO : PH–STR–01

CLIENT : SATHISH KUMAR

SITE : VANAGARAM

SHEET NO - 07
26-10-2026

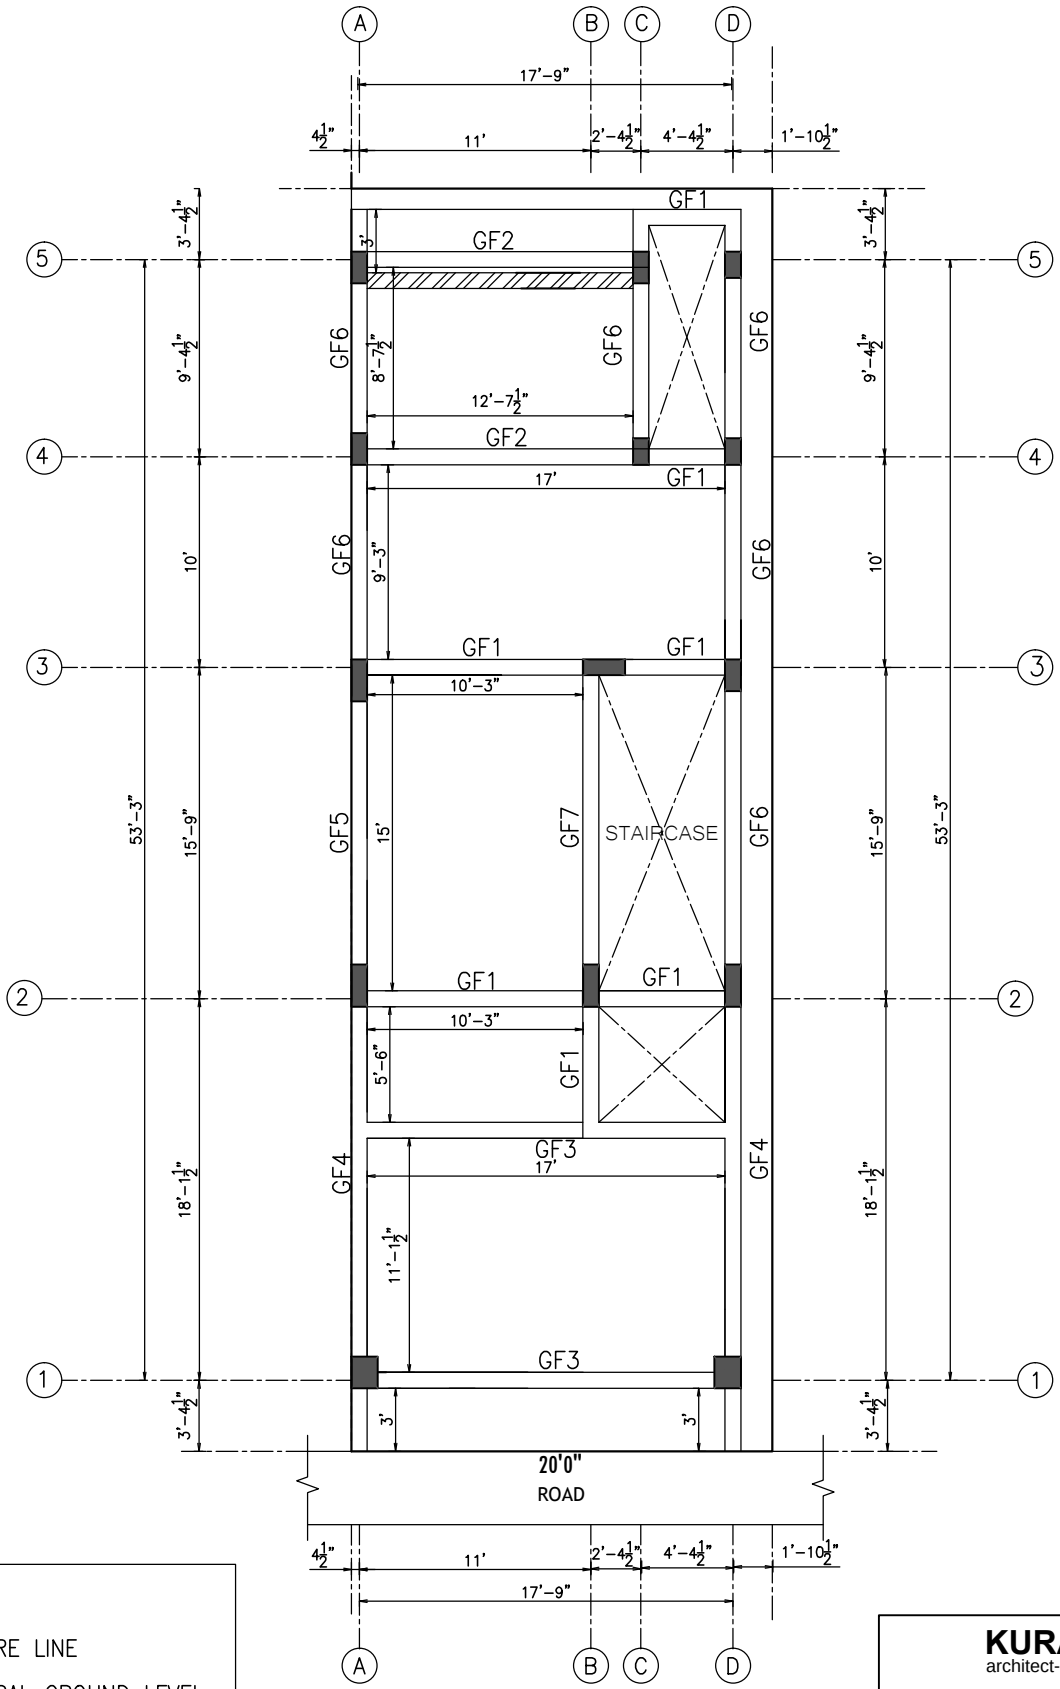



LEGEND

℄	:	CENTRE LINE
NGL	:	NATURAL GROUND LEVEL
FFL	:	FINISHED FLOOR LEVEL
TYP.	:	TYPICAL
■	:	COLUMN
——	:	COLUMN CENTERLINE
——	:	SITE BOUNDARY

LAYOUT OF GROUND FLOOR ROOF BEAM

KURAL-G
architect-engineers


JOB NO : PH–STR–01

CLIENT : SATHISH KUMAR


SITE : VANAGARAM

SHEET NO - 08


26-10-2026

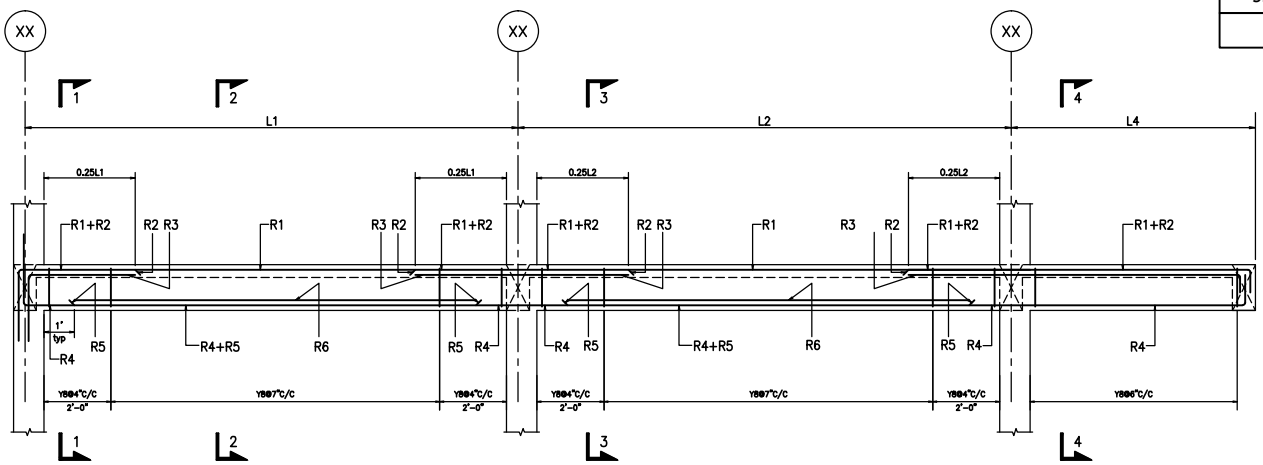


TYPICAL FLOOR BEAM DETAILS

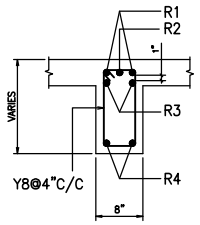


SECTION 1–1

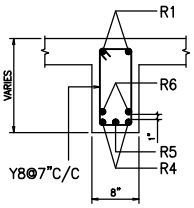


SECTION 2–2

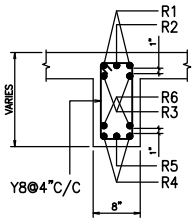


SECTION 3–3

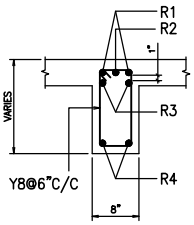


SECTION 4–4

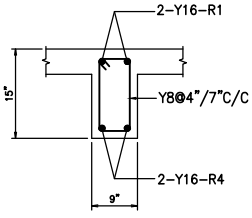


C.S OF GF1
[9"X1'–3"]

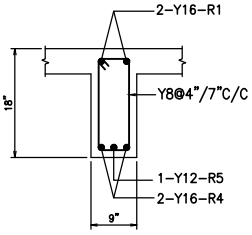


C.S OF GF2
[9"X1'–6"]

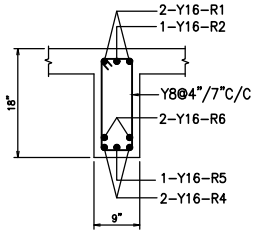


C.S OF GF3
[9"X1'–6"]

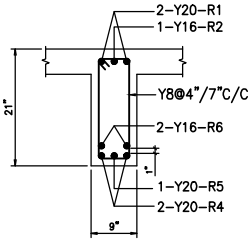


C.S OF GF4
[9"X1'–9"]

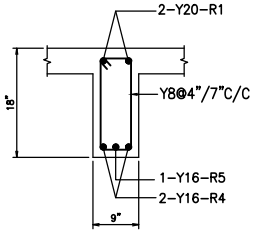


C.S OF GF5
[9"X1'–6"]

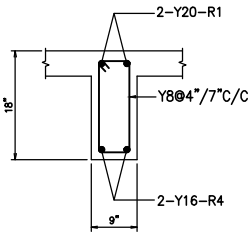

C.S OF GF6
[9"X1'–6"]

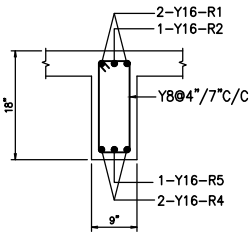

C.S OF GF7
[9"X1'–6"]

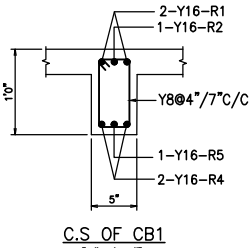

C.S OF CB1
[5"X1'–0"]



GROUND FLOOR ROOF BEAM DETAIL

KURAL-G
architect-engineers

JOB NO : PH–STR–01

CLIENT : SATHISH KUMAR

SITE : VANAGARAM


NOTE:
1. Beam column junction and main beam – secondary beam junctions must be reinforced as per miscellaneous details presented in sheet–13.
2. Clear cover = 25mm.
3. Top reinforcement shall be lapped at midspan and bottom reinforcement at support.
4. Lap length=50ø and all laps must be staggered

LEGEND
℄ : CENTRE LINE
F.F : FIRST FLOOR
S1 : SLAB–1
TYP. : TYPICAL
☒ : COLUMN TERMINATED
☒ : SUNKEN SLAB
THK. : THICKNESS OF SLAB

NOTE:
1.ARCHITECTURAL ELEVATION DRAWING MUST BE READ BEFORE CASTING THE FLOOR SLAB FOR ANY PROJECTIONS WHICH IS NOT PROVIDED IN THE STRUCTURAL DETAILS AND MUST BE CLARIFIED WITH STRUCTURAL ENGINEER.
2.ANY ARCHITECTURAL PROJECTION UPTO 6" IN SLAB CAN BE DONE WITHOUT STRUCTURAL ENGINEER'S OPINION.

NOTE:
AT INTERIOR BEAM COLUMN JUNCTIONS THE TOP REINFORCEMENT PROVIEDED MUST BE MAXIMUM OF THE TWO BEAMS MEETING AT THAT JUNCTION.

SHEET NO - 09
26-10-2026

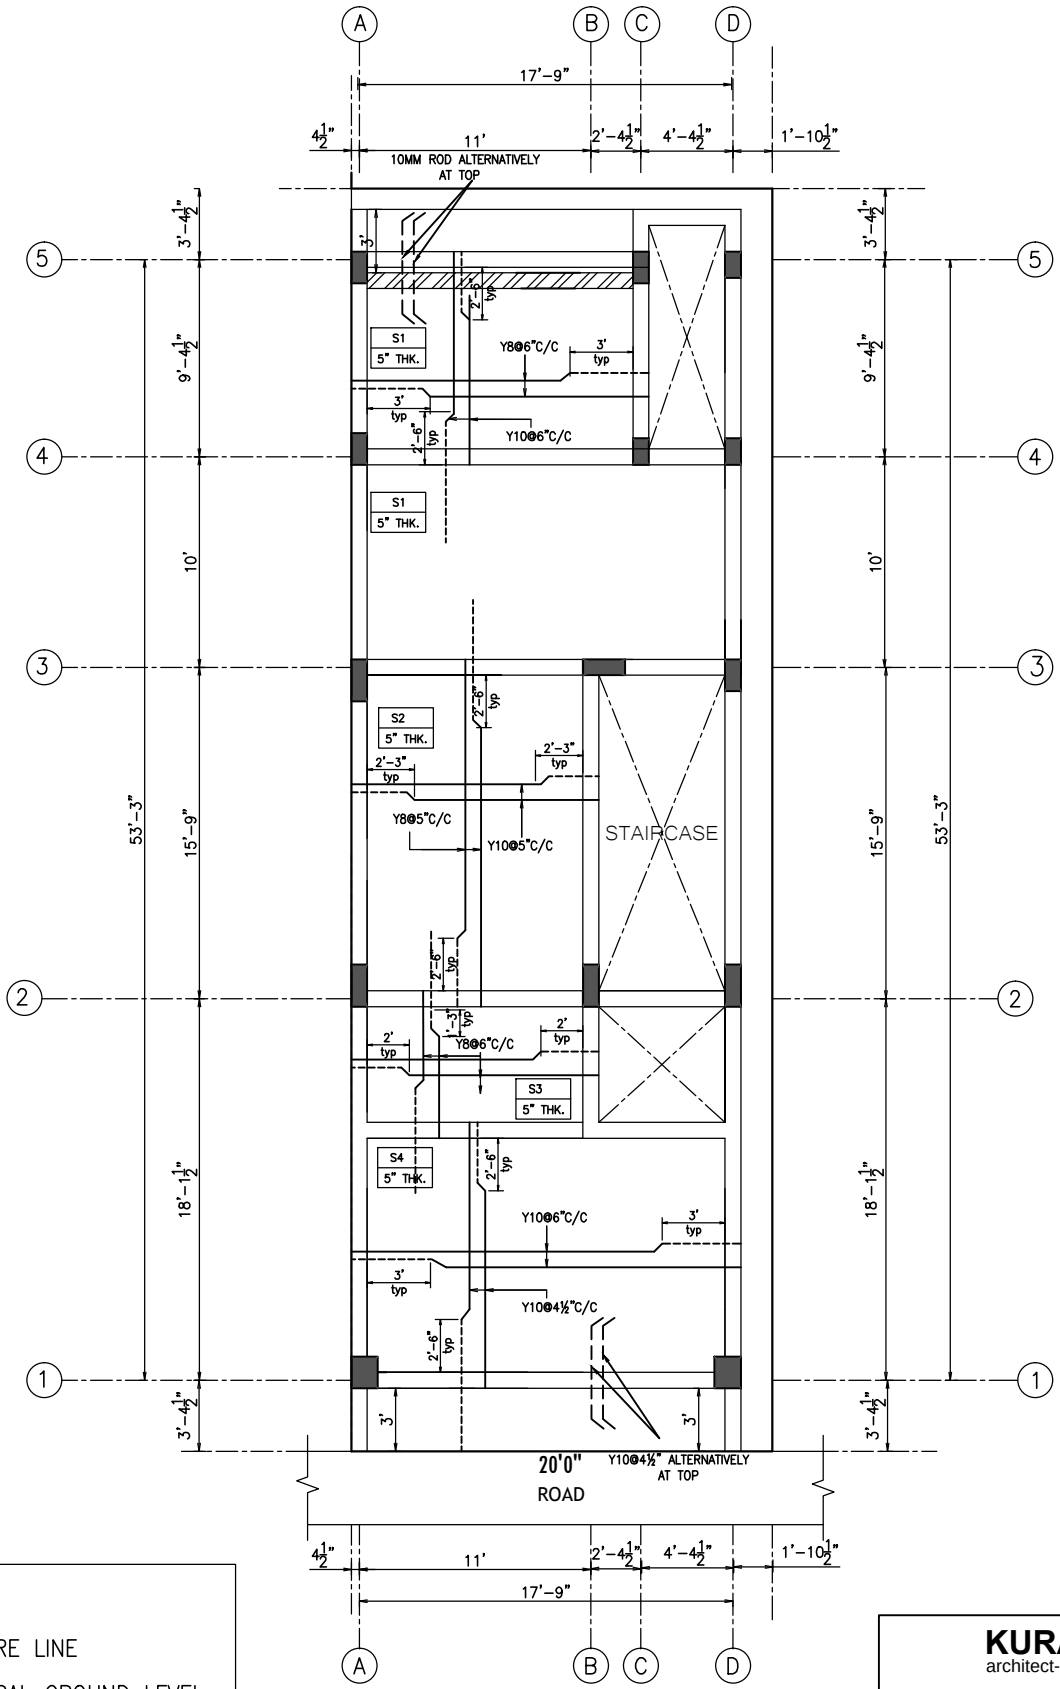



LEGEND

℄	:	CENTRE LINE
NGL	:	NATURAL GROUND LEVEL
FFL	:	FINISHED FLOOR LEVEL
TYP.	:	TYPICAL
■	:	COLUMN
——	:	COLUMN CENTERLINE
——	:	SITE BOUNDARY

LAYOUT OF GROUND FLOOR ROOF SLAB

KURAL-G
architect-engineers

JOB NO : PH–STR–01

CLIENT : SATHISH KUMAR

SITE : VANAGARAM